


FÖLDSZINTI ALAPRAJZ

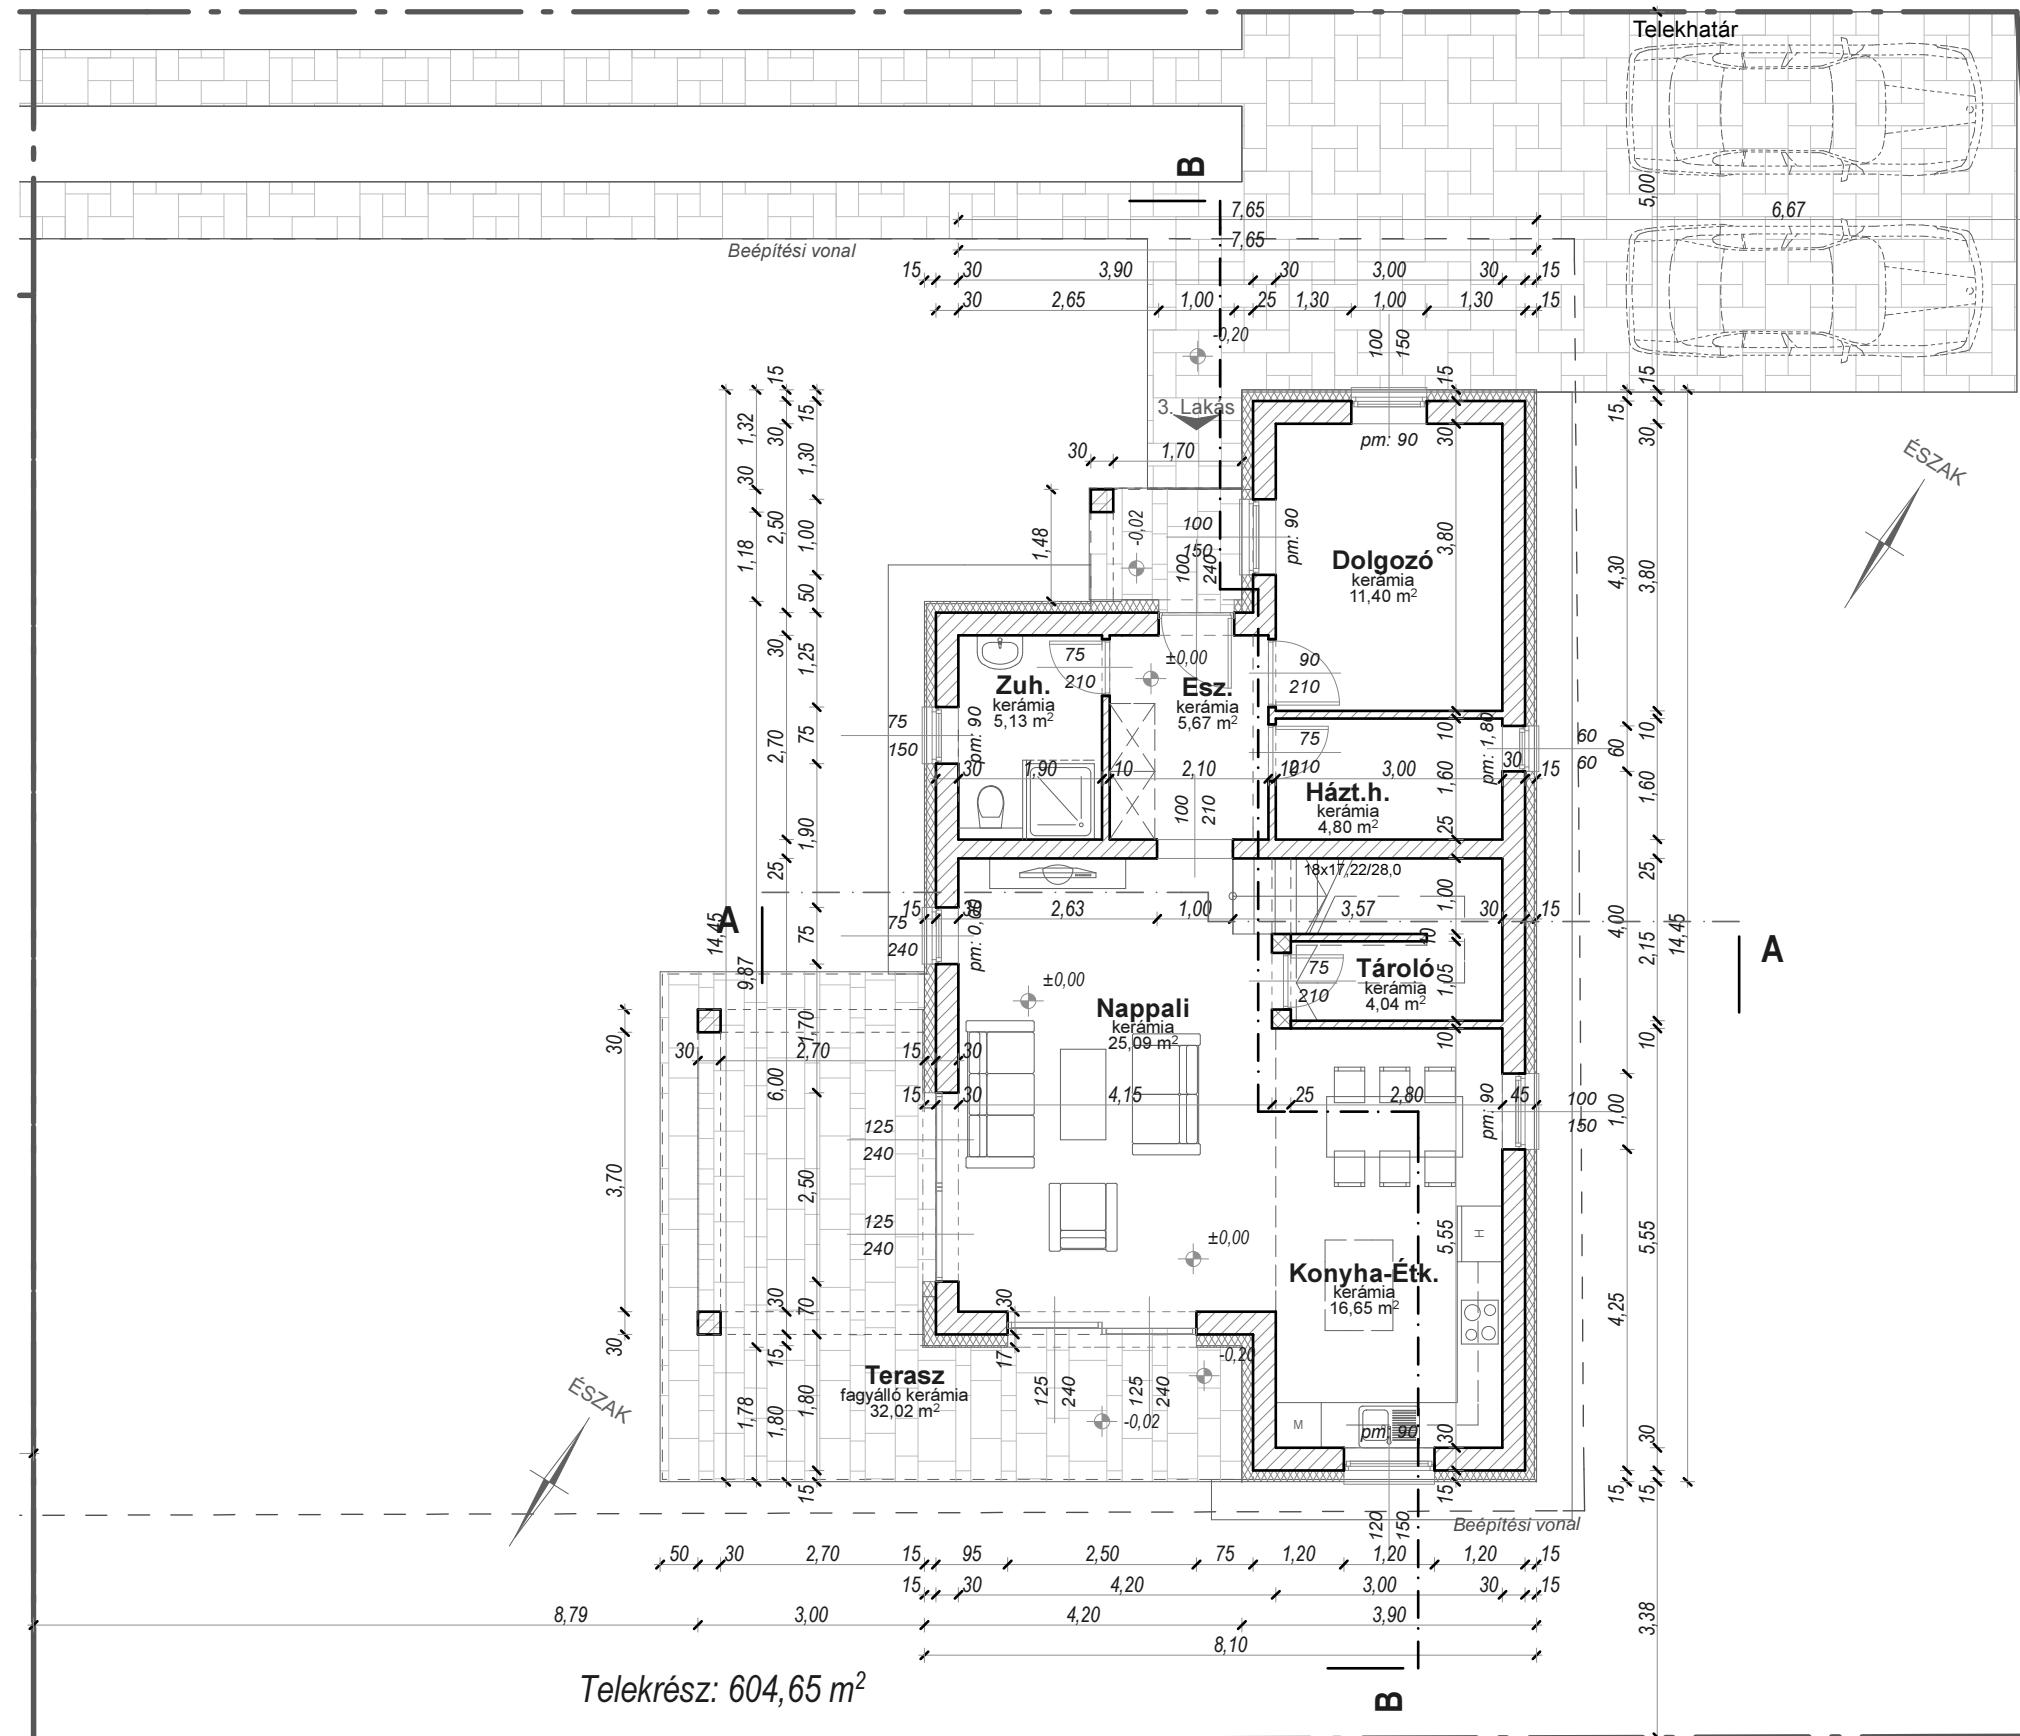

Projekt megnevezése:	EGYLAKÁSOS LAKÓÉPÜLET	
Egyesürt építés bejelentési terv		
Projekt helye:	1223 Budapest, Vilmos utca 23.	HRSZ: 228098
Tervezett:	FÖLDSZINTI ALAPRAJZ (II. ütem)	Dátum: 2021.06.14.
Tervező:	Unicsovics István (É-01-4309) 1032 Budapest, Ágoston u. 10.	Lépték: M=1:100
Beruházó:	Profitkész Kft. (Termel Katalin) 1223 Budapest, Csöngő u. 10/B.	Rajzsám: PK-ÉB-2.1