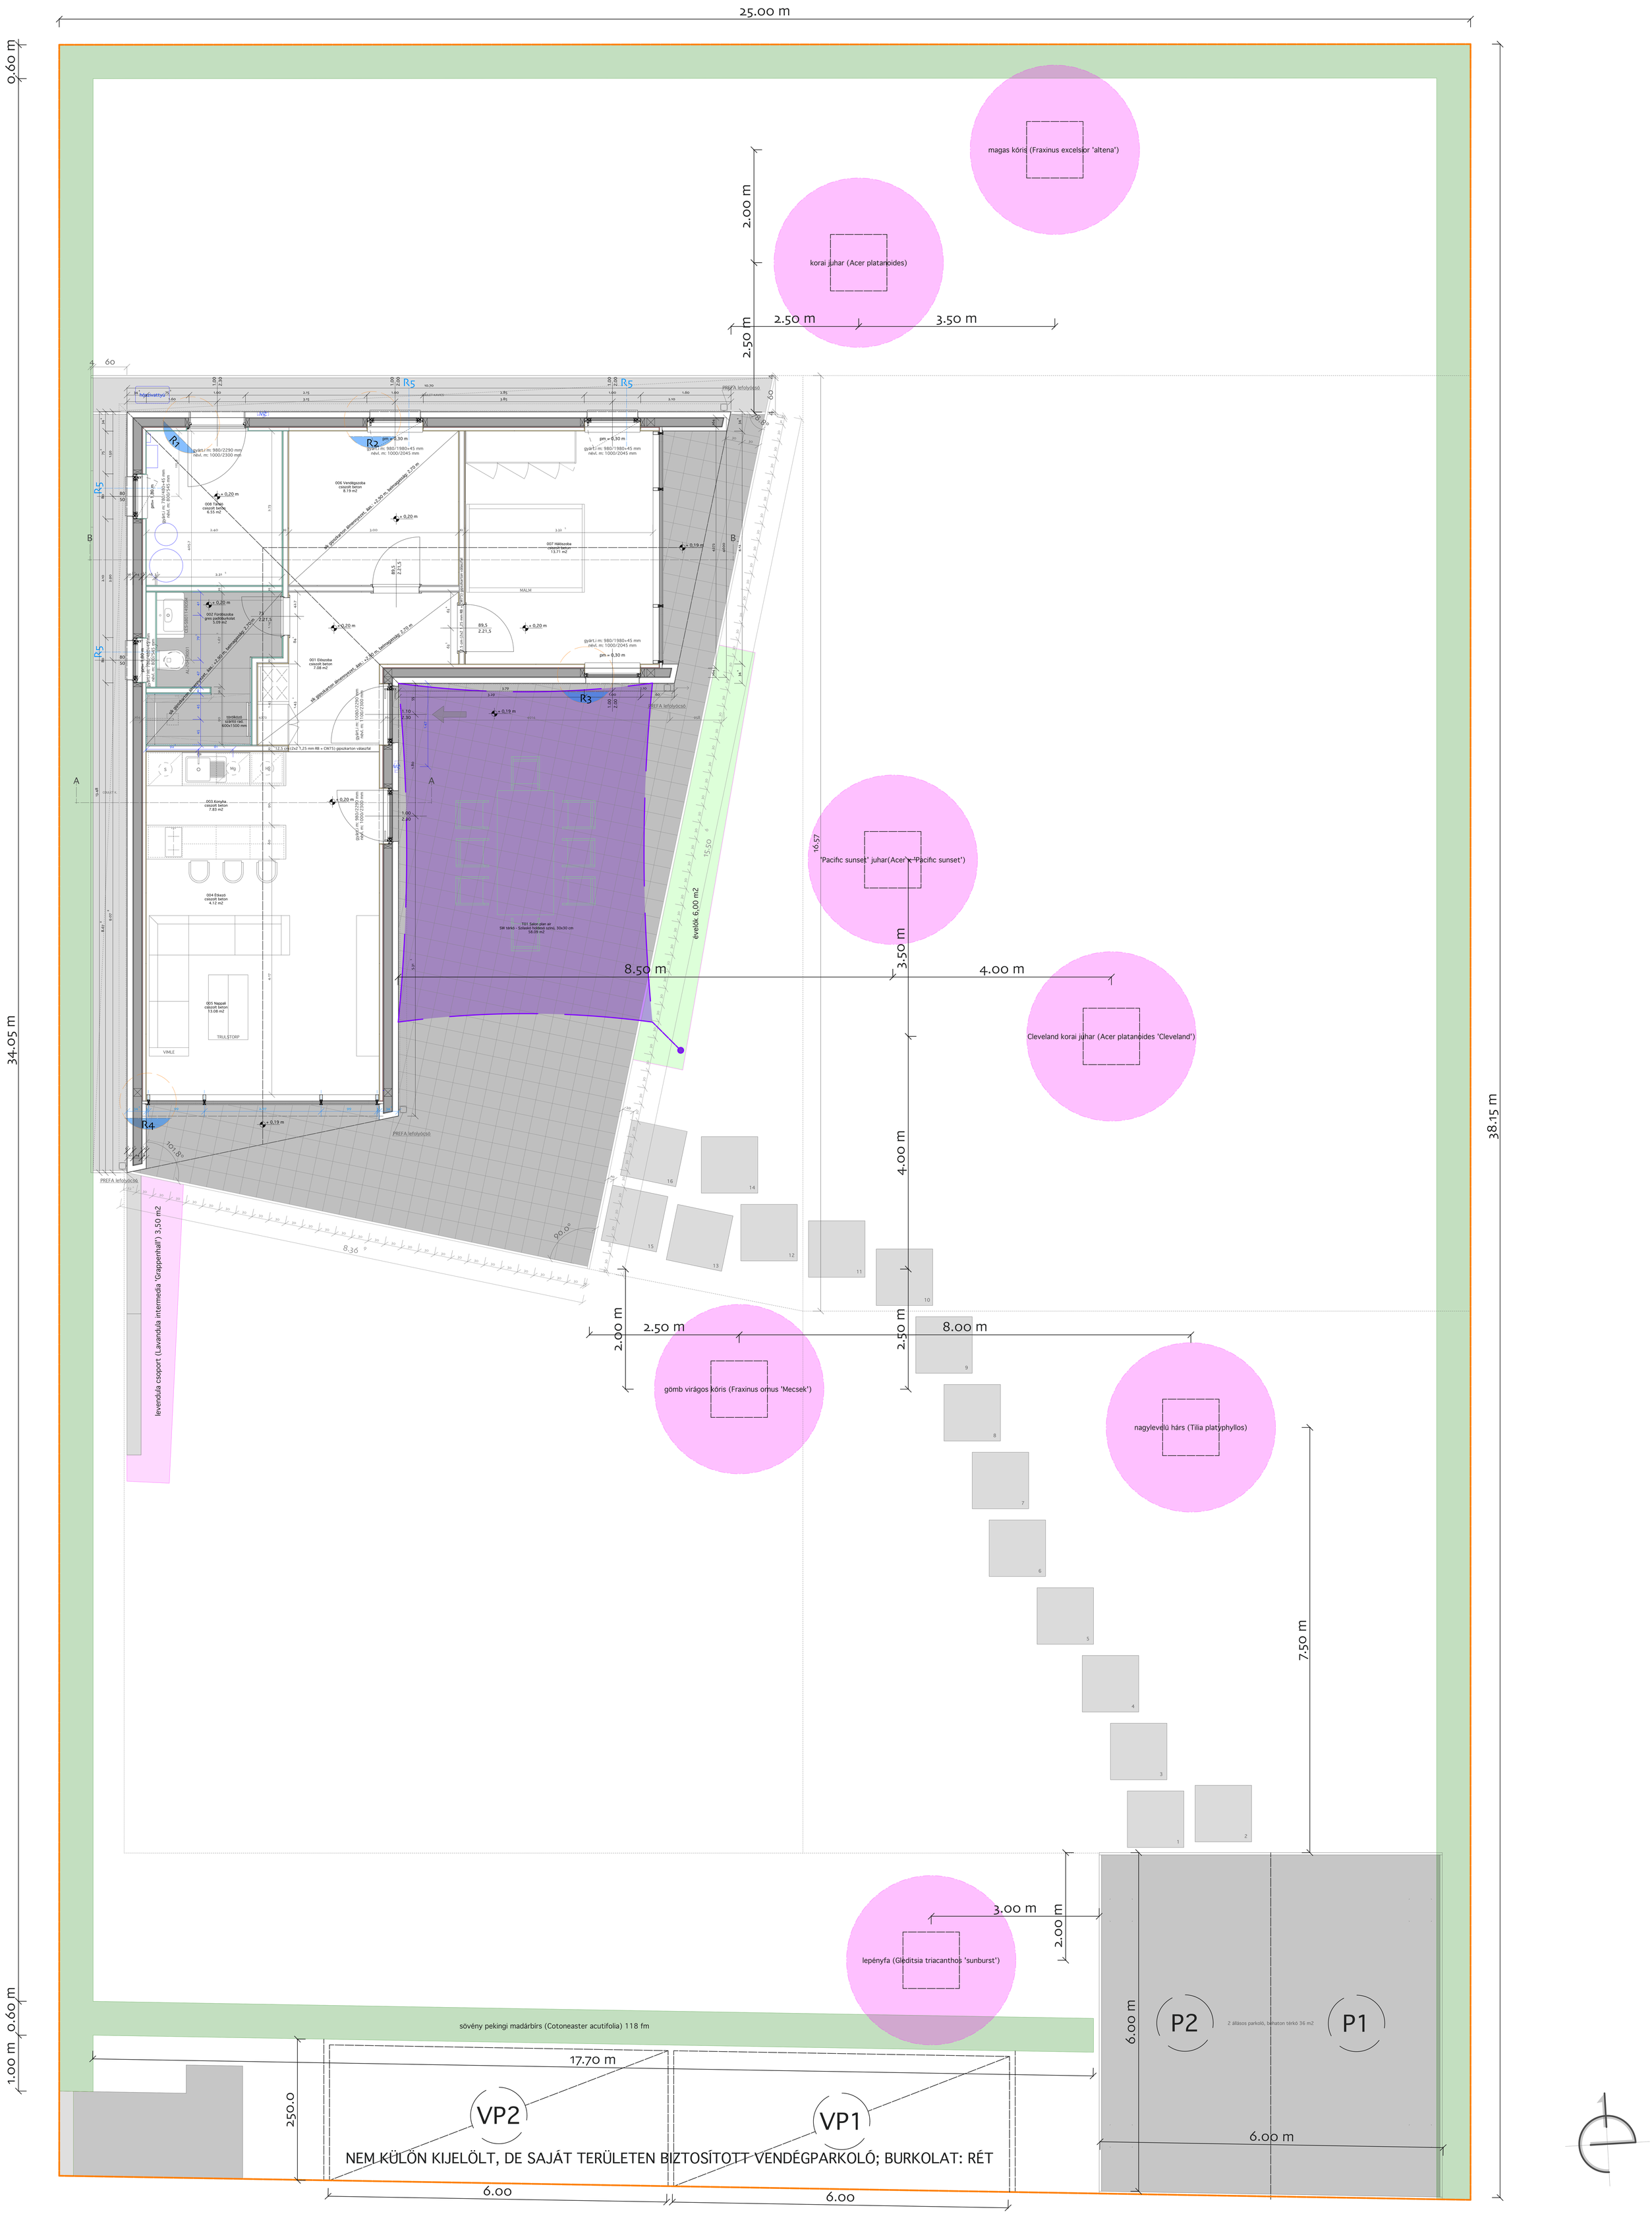
25.00 m
0.60 m
34.05 m
38.15 m
1.00 m
magas kőris (Fraxinus excelsior 'altena')
korai juhar (Acer platanoides)
2.00 m
2.50 m
3.50 m
'Pacific sunset' juhar(Acer 'Pacific sunset')
8.50 m
4.00 m
Cleveland korai juhar (Acer platanoides 'Cleveland')
gömb virágos kőris (Fraxinus ornus 'Mecsek')
8.00 m
nagylevelű hárs (Tilia platyphyllos)
7.50 m
levendula csoport (Lavandula intermedia 'Grappenhall') 3.50 m2
évelők 6.00 m2
lepényfa (Gleditsia triacanthos 'sunburst')
3.00 m
sövény pekingi madárbírs (Cotoneaster acutifolia) 118 fm
P1
P2
2 állásos parkoló, behaton térkő 36 m2
6.00 m
17.70 m
250.0
VP1
VP2
6.00
NEM KÜLÖN KIJELÖLT, DE SAJÁT TERÜLETEN BIZTOSÍTOTT VENDÉGPARKOLÓ; BURKOLAT: RÉT